





Maßstab 1:100

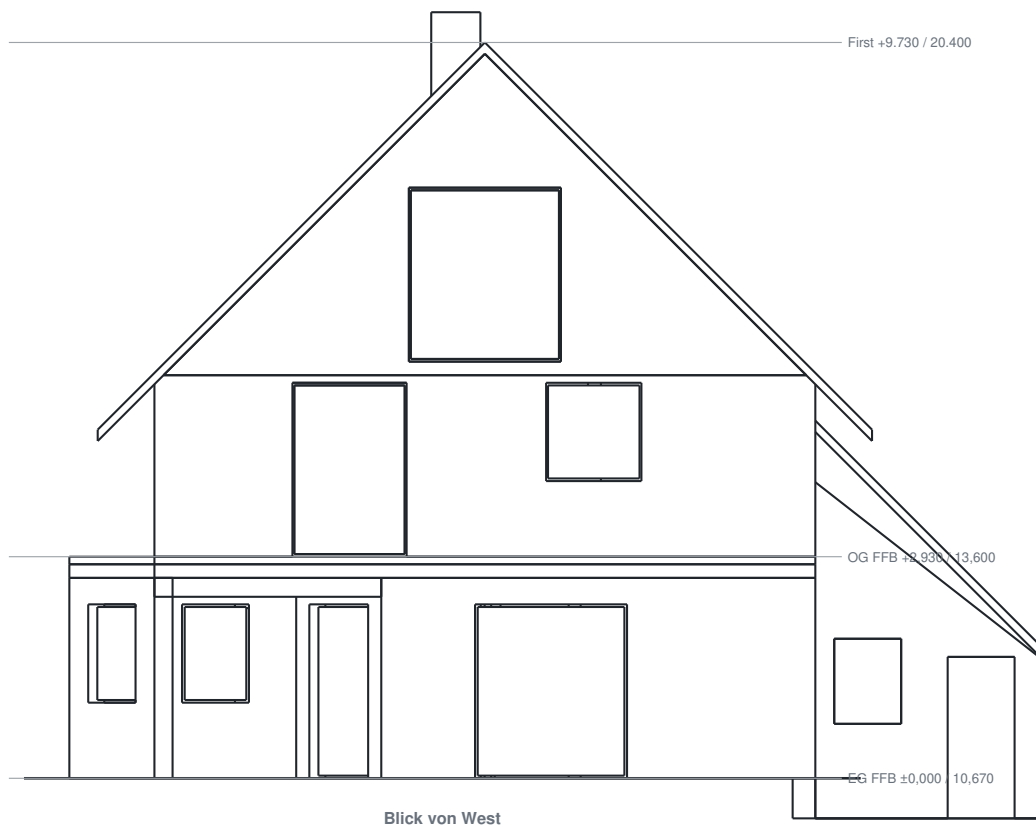

Ansicht West 1:100

Bauprojekt: Wohnhaus — Dachausbau, Variante 3

Planverfasser: Bruno Enslinger, Architekt

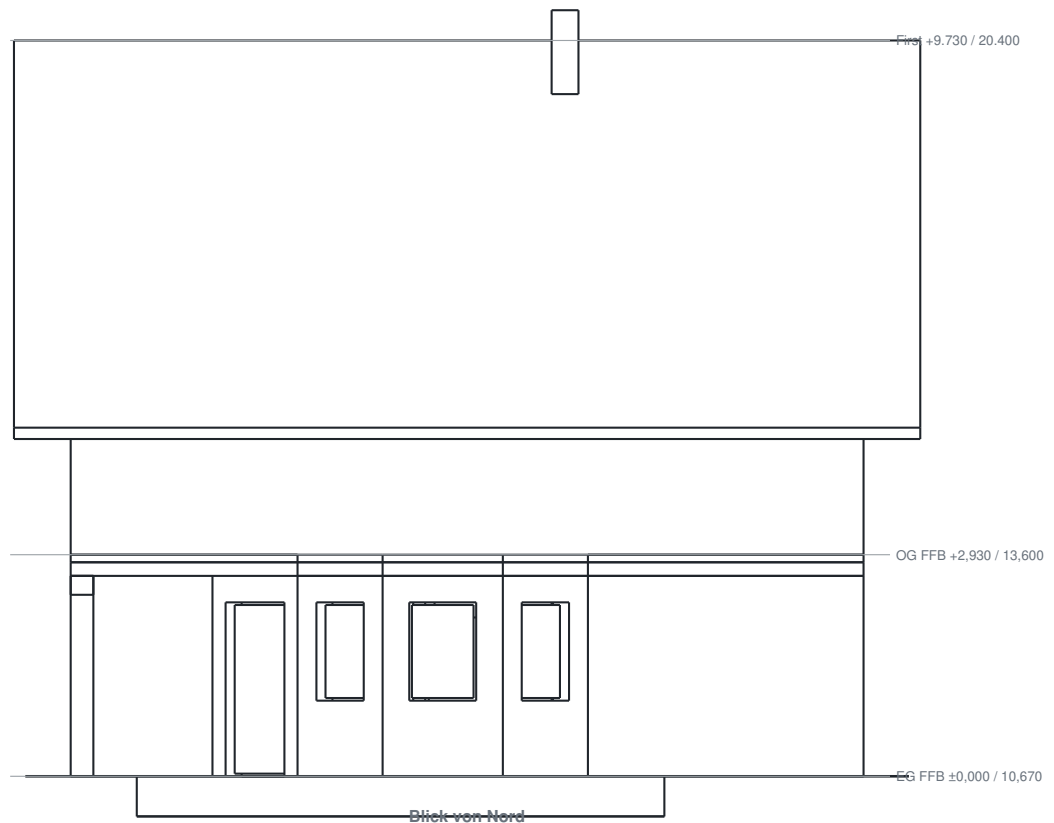

Maßstab 1:100



Ansicht Nord 1:100

Bauprojekt: Wohnhaus — Dachausbau, Variante 3

Planverfasser: Bruno Ensinger, Architekt




Maßstab 1:100



Ansicht Ost 1:100

Bauprojekt: Wohnhaus — Dachausbau, Variante 3

Planverfasser: Bruno Ensinger, Architekt

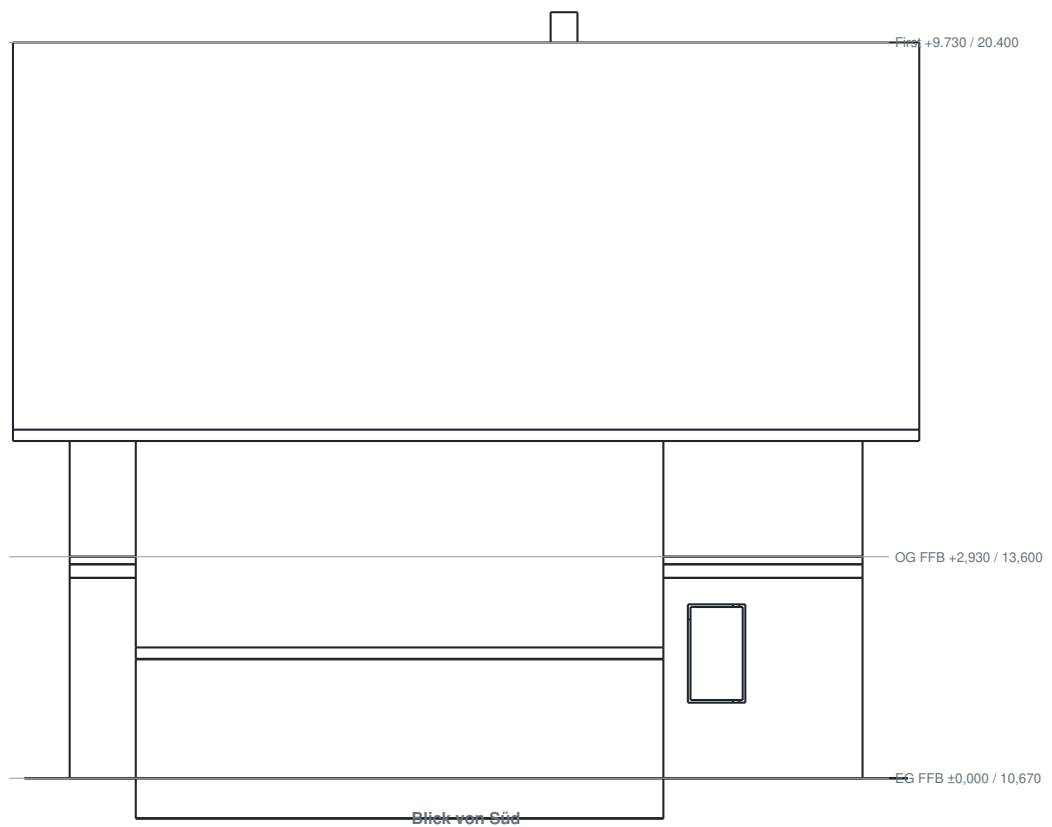


Maßstab 1:100



Ansicht Süd 1:100

Bauprojekt: Wohnhaus — Dachausbau, Variante 3


Planverfasser: Bruno Ensminger, Architekt

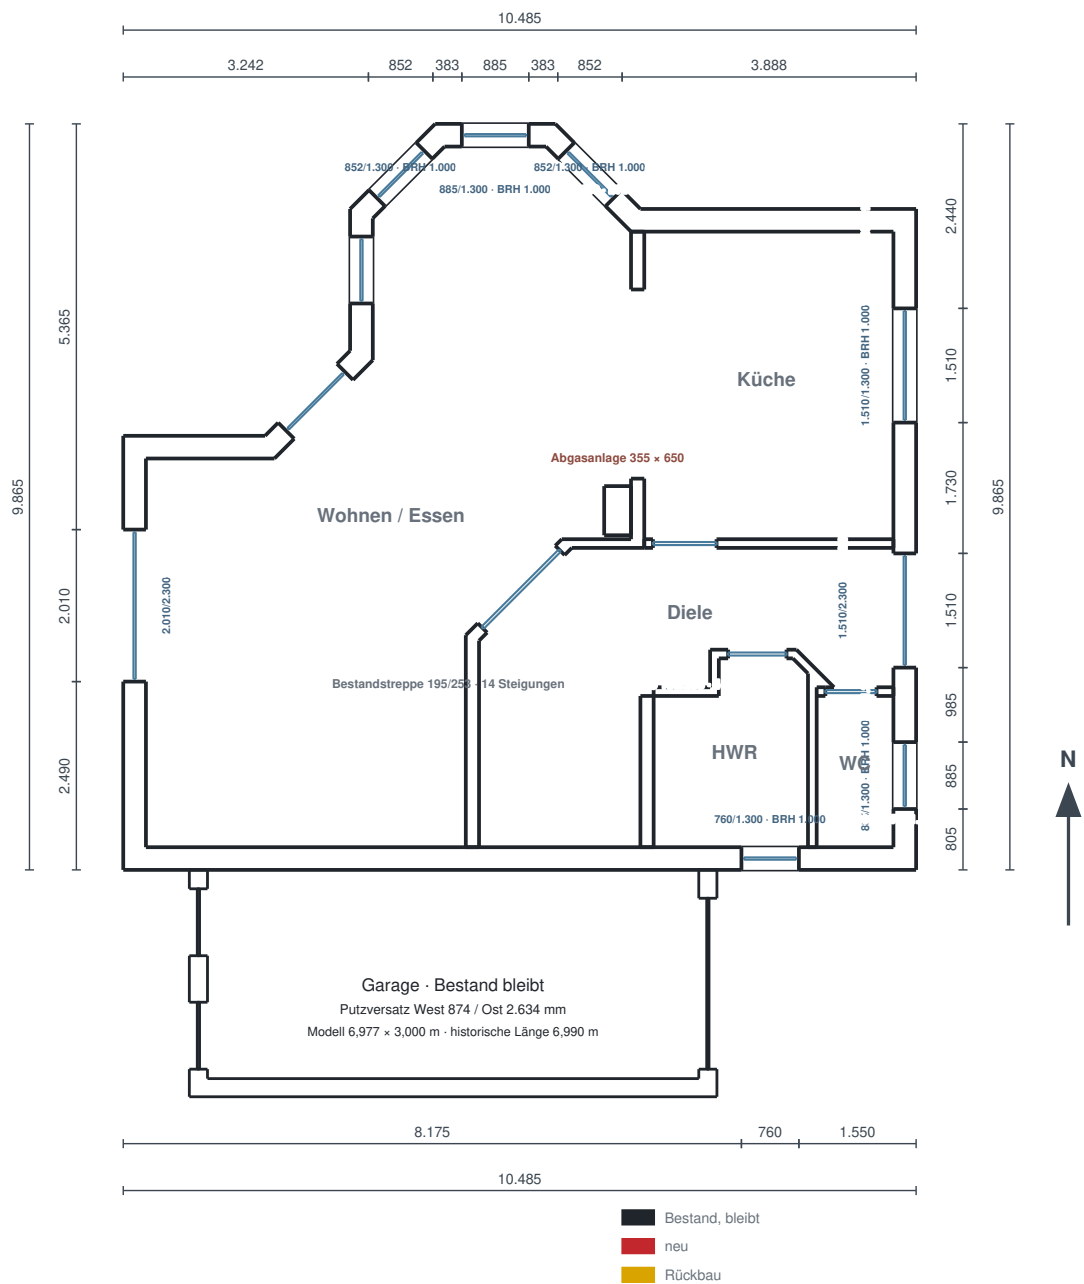

Maßstab 1:100



Grundriss EG 1:100

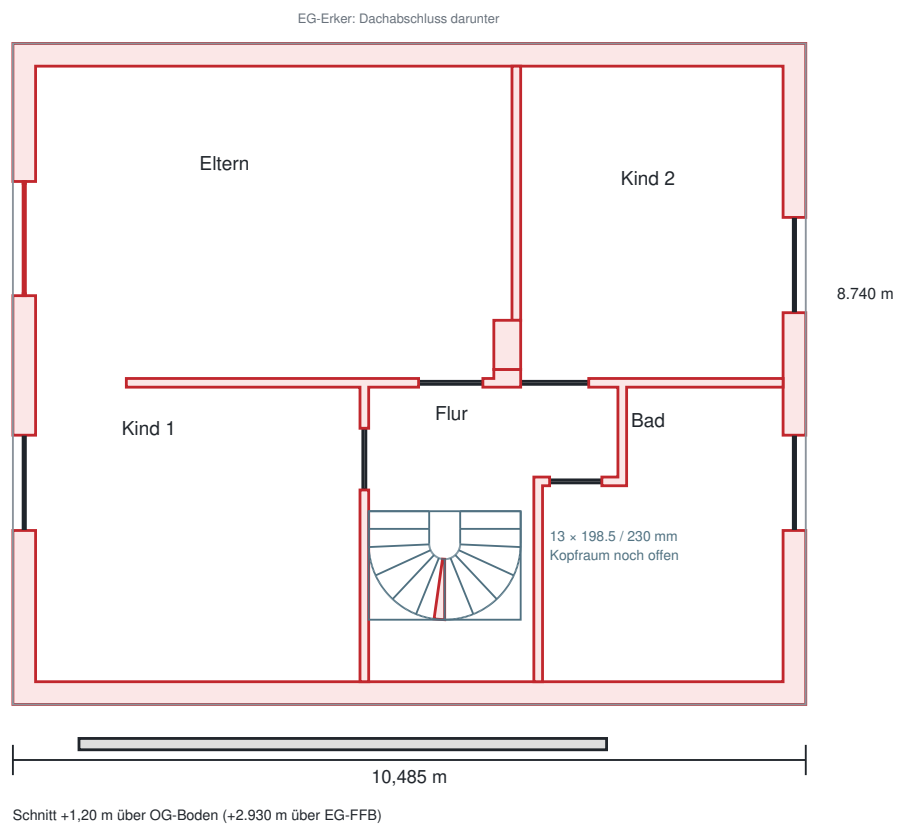


Maßstab 1:100



Grundriss OG 1:100

Bauprojekt: Wohnhaus — Dachausbau, Variante 3

Planverfasser: Bruno Ensinger, Architekt

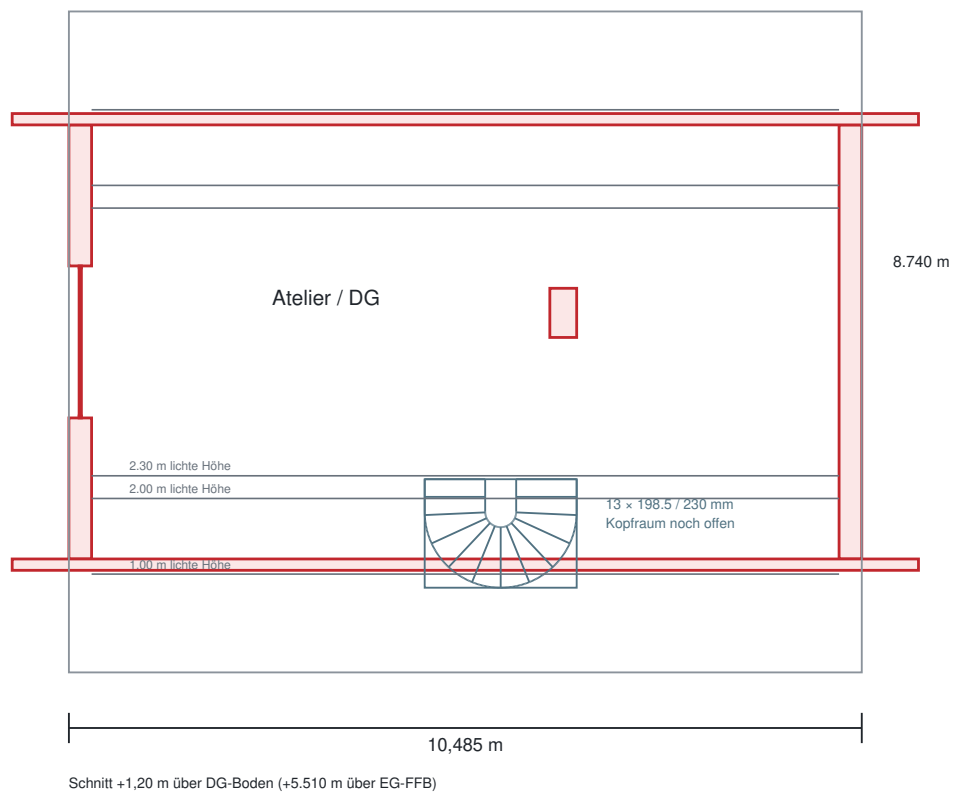


Maßstab 1:100



Grundriss DG 1:100

Bauprojekt: Wohnhaus — Dachausbau, Variante 3

Planverfasser: Bruno Ensinger, Architekt

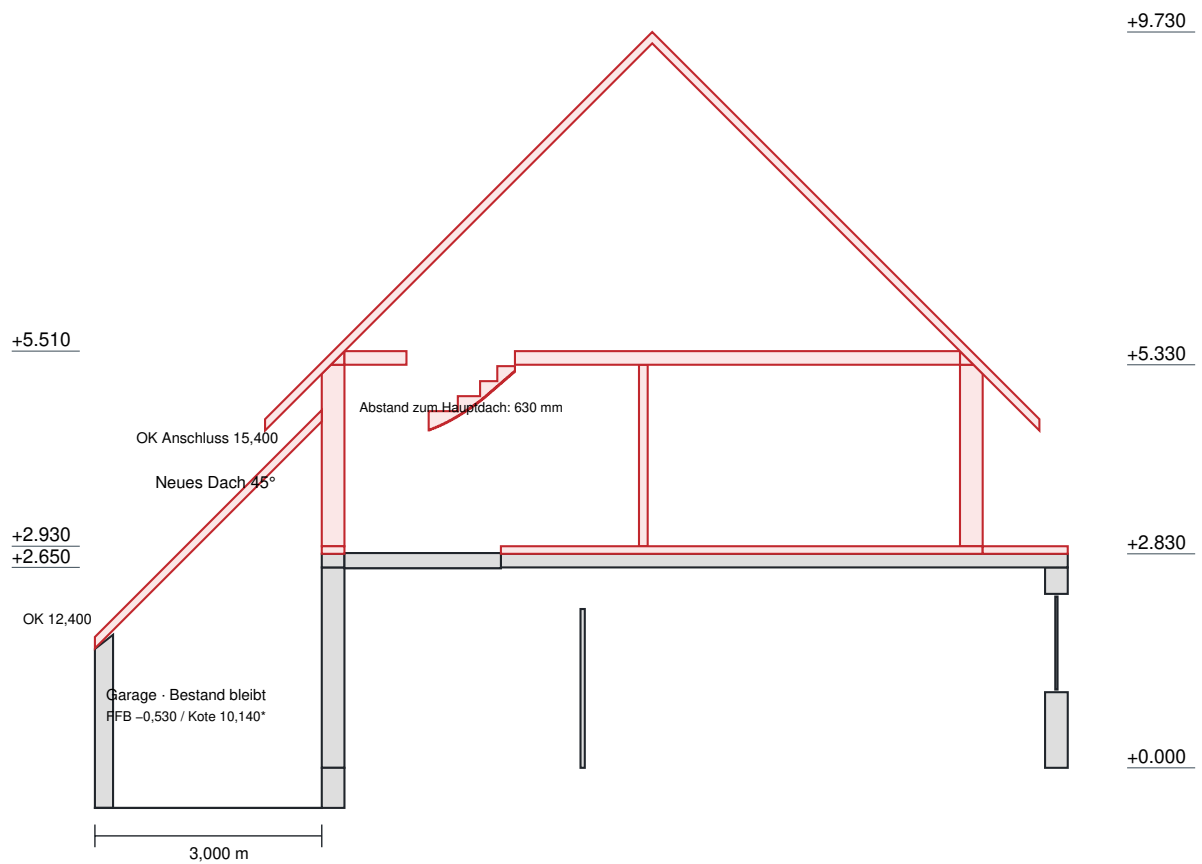

Schnittebene X = 5.000 m · Höhen relativ zu EG-FFB; absolute Koten separat
 Schwarz: verbleibender Bestand · Rot: Planung · Maße in m
 Garage: Dachschichten und seitlicher Abschluss offen; keine Aufmauerung modelliert.
 * Garagen-FFB aus Schnitt; abweichend lesbare EG-Kote bleibt offen. Boden nur Oberflächenproxy.
 OG → Atelier: 2.580 m · 13 Steigungen × 198.5 mm; Treppeneignung offen.


Maßstab 1:100



Querschnitt 1:100

Bauprojekt: Wohnhaus — Dachausbau, Variante 3

Planverfasser: Bruno Enslinger, Architekt

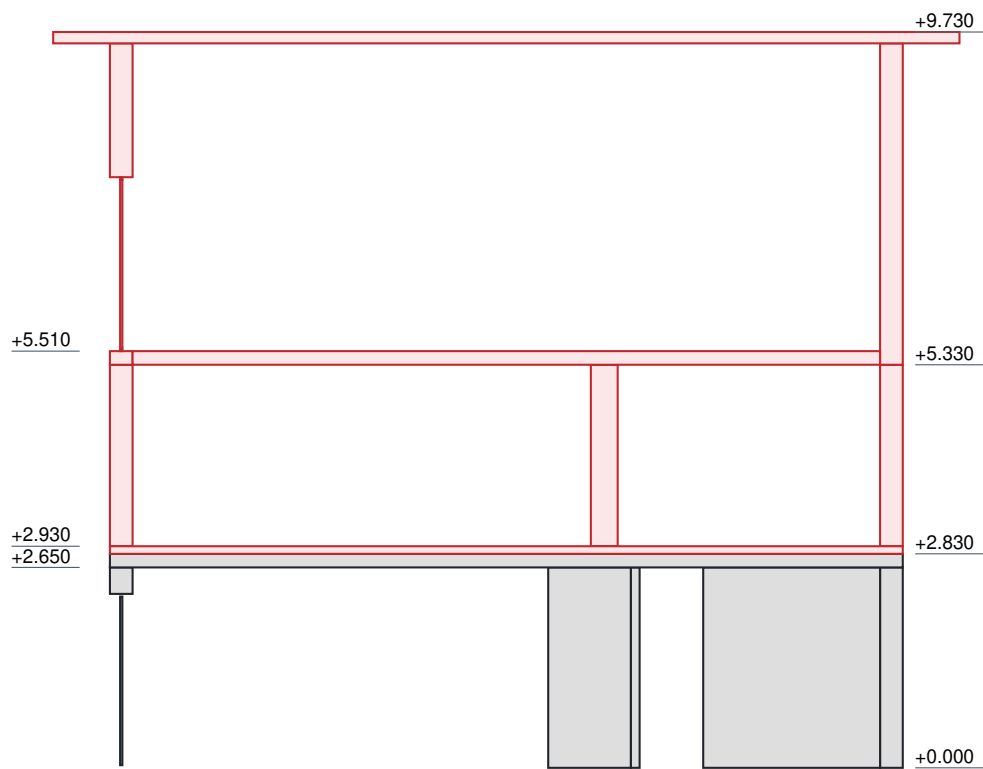

Schnittebene Y = 4.370 m · Höhen relativ zu EG-FFB; absolute Koten separat
 Schwarz: verbleibender Bestand · Rot: Planung · Maße in m
 Garage: Dachschichten und seitlicher Abschluss offen; keine Aufmauerung modelliert.
 * Garagen-FFB aus Schnitt; abweichend lesbare EG-Kote bleibt offen. Boden nur Oberflächenproxy.
 OG → Atelier: 2.580 m · 13 Steigungen × 198.5 mm; Treppeneignung offen.

Maßstab 1:100



Längsschnitt 1:100

Bauprojekt: Wohnhaus — Dachausbau, Variante 3

Planverfasser: Bruno Ensinger, Architekt