


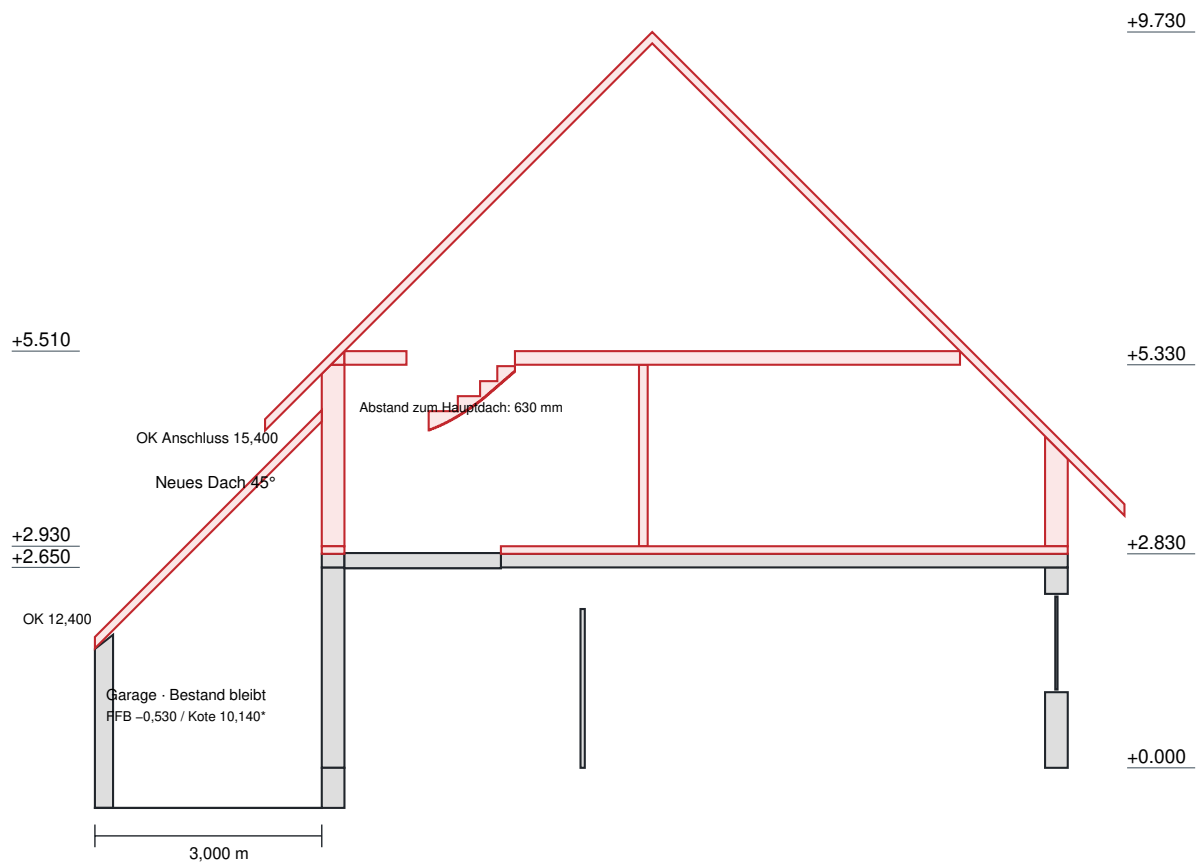

Schnittebene X = 5.000 m · Höhen relativ zu EG-FFB; absolute Koten separat
 Schwarz: verbleibender Bestand · Rot: Planung · Maße in m
 Garage: Dachschichten und seitlicher Abschluss offen; keine Aufmauerung modelliert.
 * Garagen-FFB aus Schnitt; abweichend lesbare EG-Kote bleibt offen. Boden nur Oberflächenproxy.
 OG → Atelier: 2.580 m · 13 Steigungen x 198.5 mm; Treppeneigung offen.

Maßstab 1:100



Querschnitt 1:100

Bauprojekt: Wohnhaus — Dachausbau, Variante 4

Planverfasser: Bruno Ensinger, Architekt