


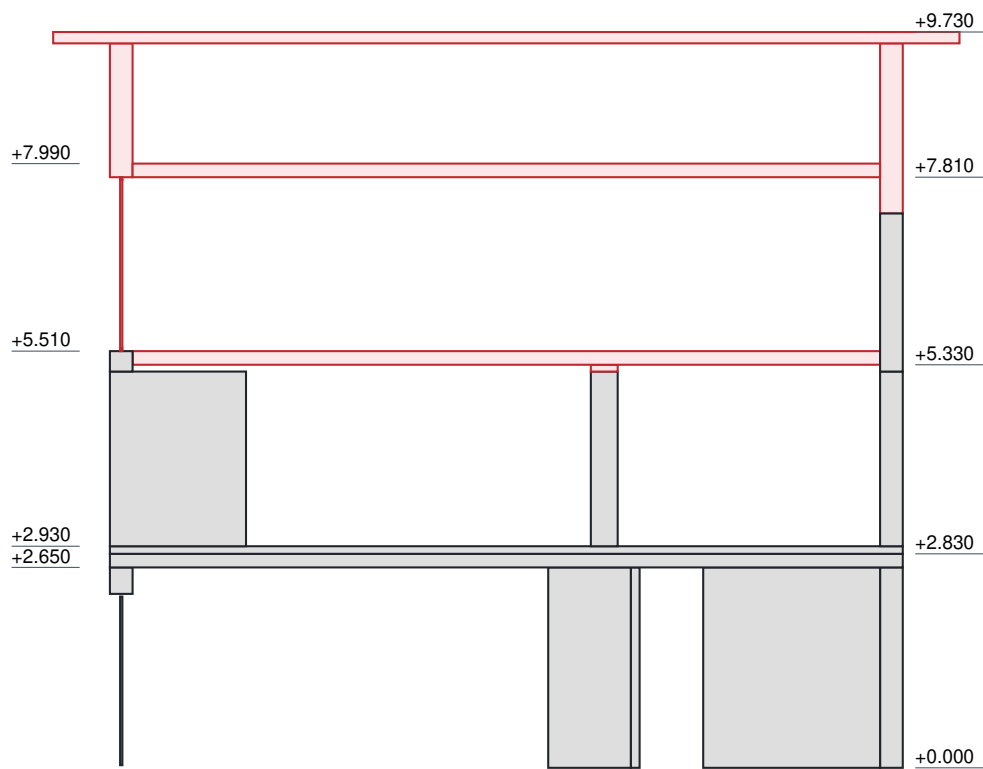

Schnittebene Y = 4.370 m · Höhen relativ zu EG-FFB; absolute Koten separat
 Schwarz: verbleibender Bestand · Rot: Planung · Maße in m
 Garage: Dachschichten und seitlicher Abschluss offen; keine Aufmauerung modelliert.
 * Garagen-FFB aus Schnitt; abweichend lesbare EG-Kote bleibt offen. Boden nur Oberflächenproxy.
 OG → Atelier: 2.580 m · 12 Steigungen × 215.0 mm; Treppeneignung offen.

Maßstab 1:100



Längsschnitt 1:100

Bauprojekt: Wohnhaus — Dachausbau, Variante 5

Planverfasser: Bruno Ensinger, Architekt